A2	PROSOIL	BOREHOLE NO: BH-1	
		LOCATION : Nona Danga, Bagerhat Sadar, Bagerhat.	
PROJECT : MULTI PURPOSE CYCLONE SHELTER.		DEPTH OF BORING : 18.0m	R. L.: 0.30m below from Road Level.
CLIENT : US Army Corps of Engineers,Pacific Ocean Division.		DATE OF BORING : 02-01-2009.	G. W. T : 1.52m below from E. G. L.

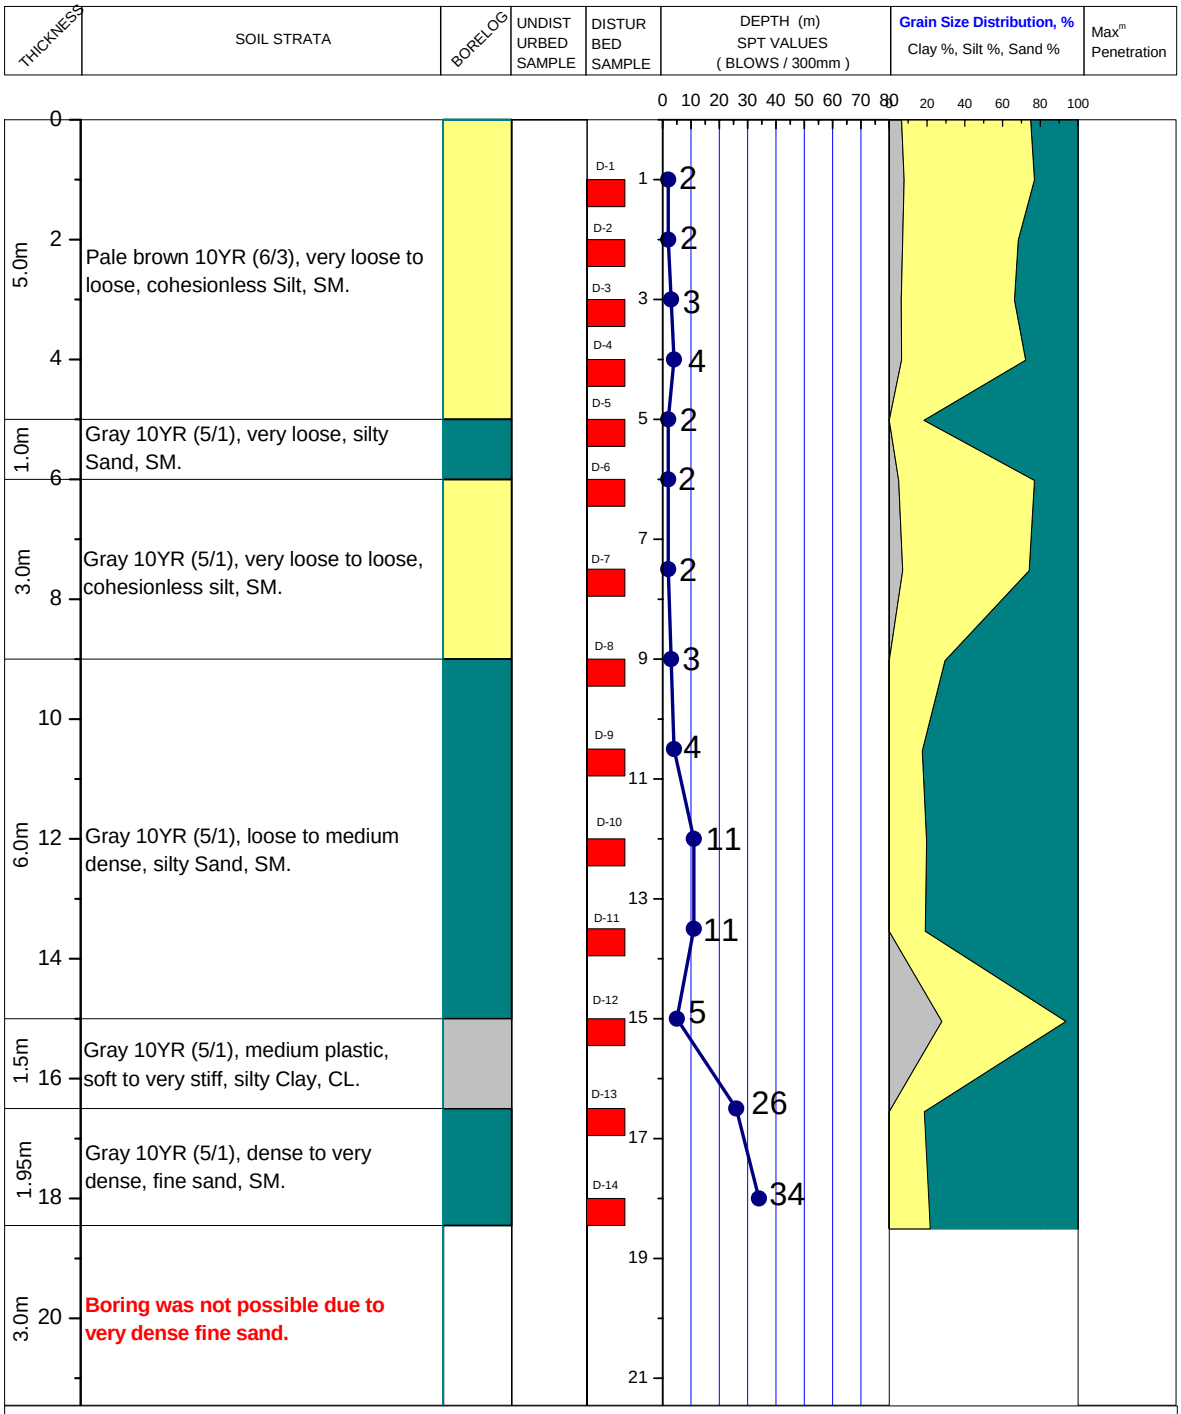

LEGEND FOR BORELOG AND GRAIN SIZE DISTRIBUTION

PLASTIC SILTY CLAY

LOW PLASTIC CLAYEY SILT

NON PLASTIC SILT

SAND

ORGANIC

UNDISTURBED SAMPLE

DISTURBED SAMPLE

SHALE

N- BLOWS DELIVERED PER FOOT BY A 140 LB HAMMER FALLING 30 INCHES

MAX^{m} PENETRATION= 50 BLOWS

AFTER 50 BLOWS PENETRATION DEPTH WERE MEASURED