A2	PROSOIL	BOREHOLE NO: BH-1	
		LOCATION : 4th km (CH-3Km+50.97m) of Dhaka-Chittagong Trank Road.	
PROJECT : Proposed Shashangacha Flyover.		DEPTH OF BORING : 45.0m	Chainage: 3km+50.97m R. L. : 9.2
CLIENT : Road Division,Comilla.		DATE OF BORING : 13-07-2010.	G. W. T : 1.8m below from E.G.L.

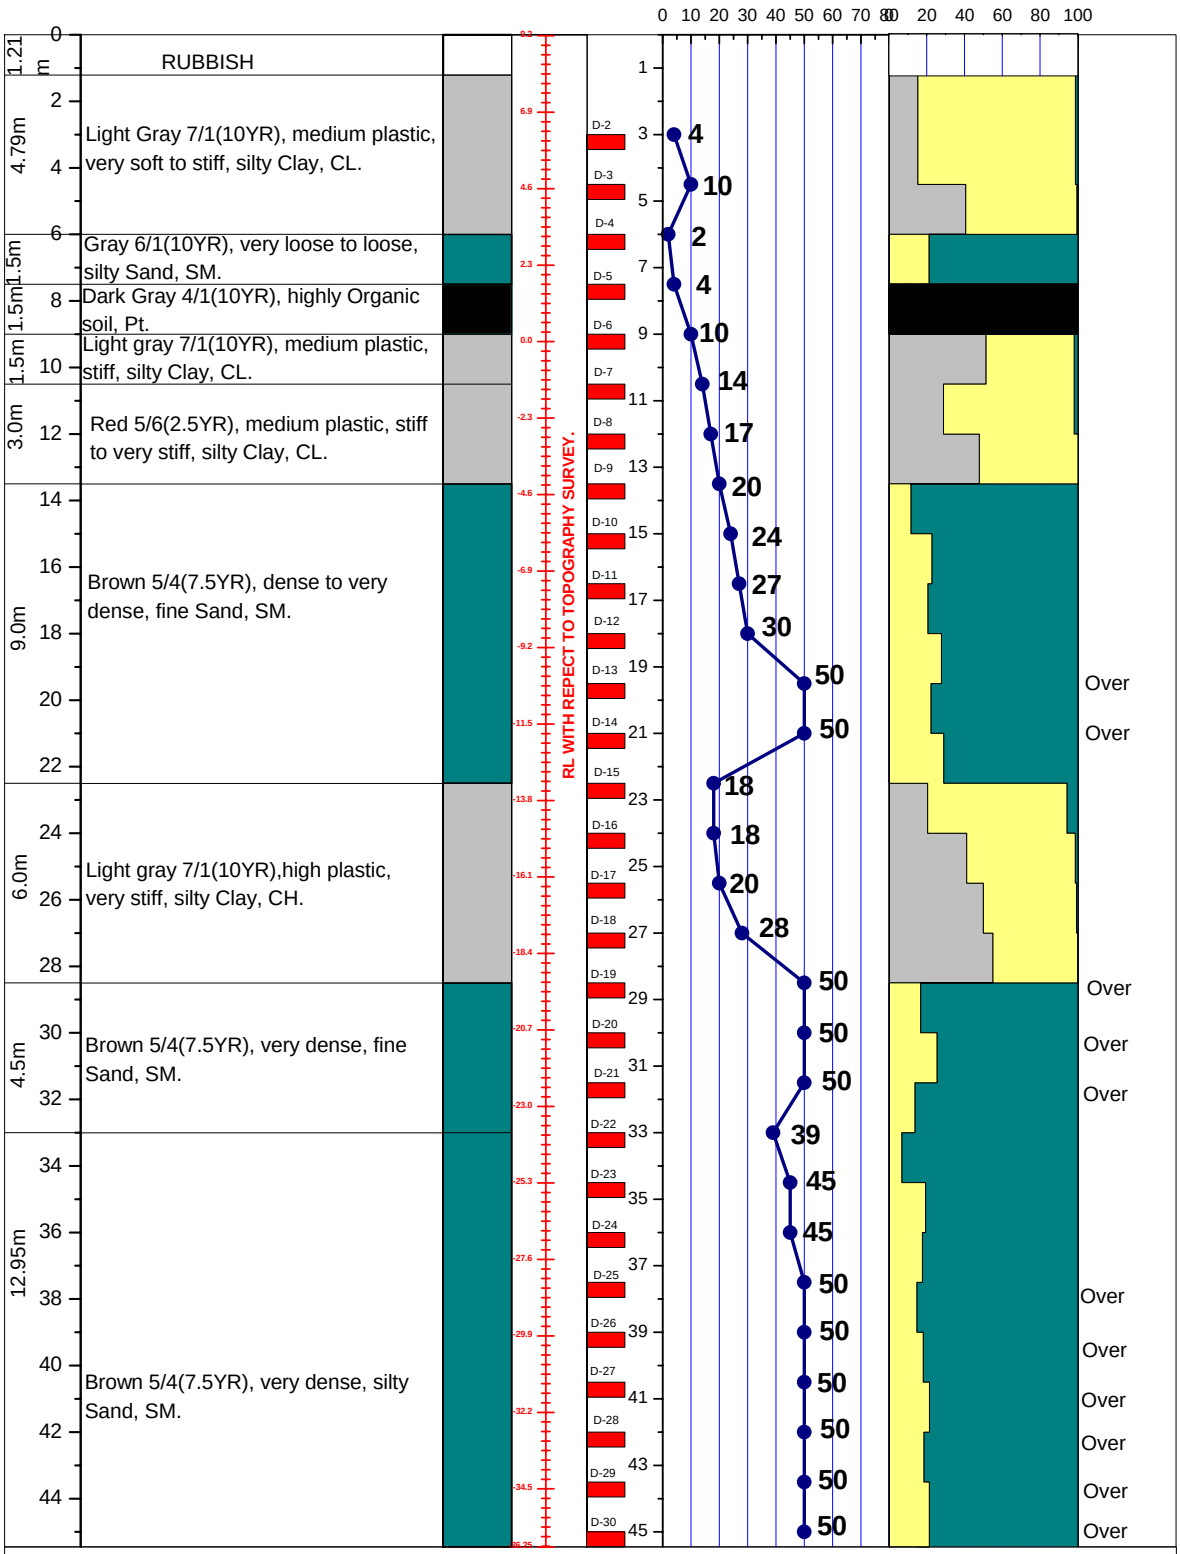

LEGEND FOR BORELOG AND GRAIN SIZE DISTRIBUTION (BASED ON 'ASTM CLASSIFICATION D-2487')

PLASTIC CLAY	SILT	PEAT/HIGHLY ORGANIC SOIL	UNDISTURBED SAMPLE
MICACEOUS FINE SAND/SILT	SAND	SHALE	DISTURBED SAMPLE

N- BLOWS DELIVERED PER FOOT BY A 140 LB HAMMER FALLING 30 INCHES

MAX^m PENETRATION= 50 BLOWS. AFTER 50 BLOWS PENETRATION DEPTH WERE MEASURED