A2	Tarique Hasan & Associates Ltd.	BOREHOLE NO: 12	Easting: 222823.00	Northing: 2523856.00
		LOCATION : Barisal Airport, Barisal.		
PROJECT : Consultant Services for Development of Saidpur, Barisal and Osmani International Airport Projects (Design Phase)		DEPTH OF BORING : 18.0m		R. L. : 1.825m
CLIENT : Civil Aviation Authority of Bangladesh.		DATE OF BORING : 28-09-2018		B. W. T : 1.0 m below from E. G. L.

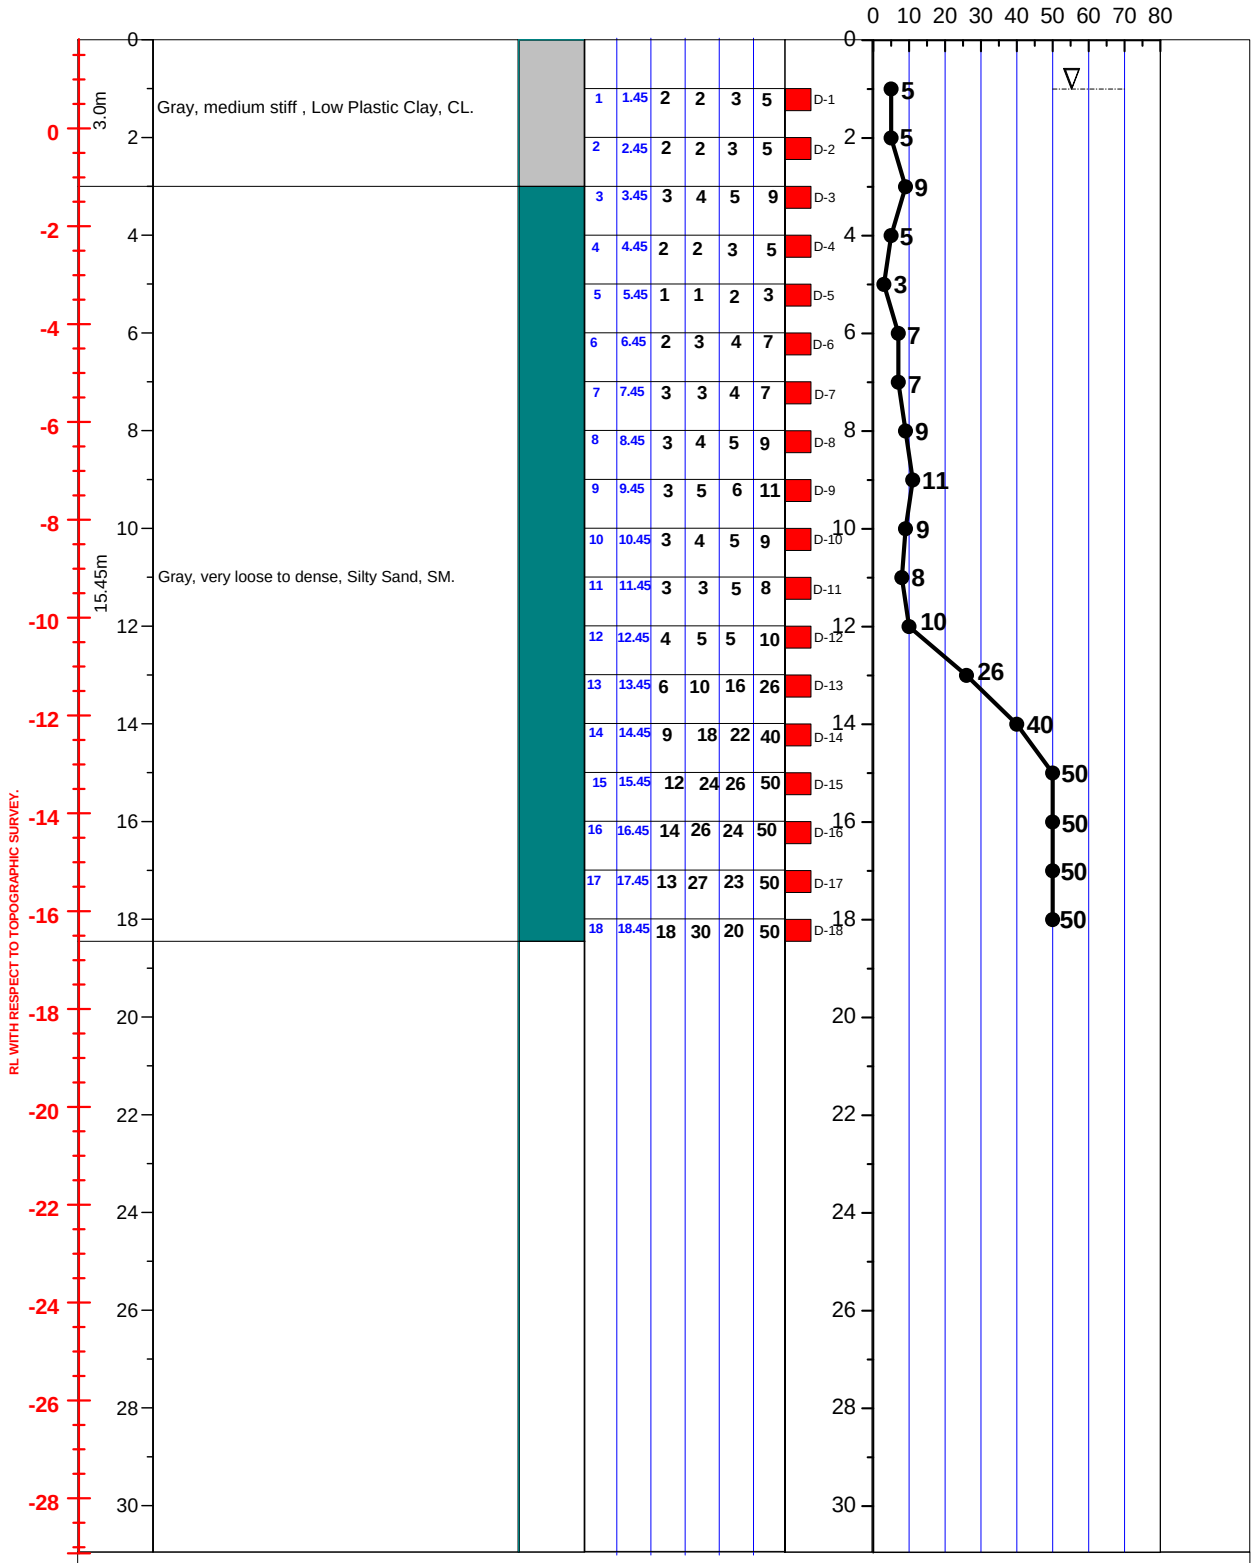

	FROM (m)	TO (m)	N1=150 (mm)	N2=300 (mm)	N3=450 (mm)	N=N2+N3	DISTURBED SAMPLE
1	1.45		2	2	3	5	D-1
2	2.45		2	2	3	5	D-2
3	3.45		3	4	5	9	D-3
4	4.45		2	2	3	5	D-4
5	5.45		1	1	2	3	D-5
6	6.45		2	3	4	7	D-6
7	7.45		3	3	4	7	D-7
8	8.45		3	4	5	9	D-8
9	9.45		3	5	6	11	D-9
10	10.45		3	4	5	9	D-10
11	11.45		3	3	5	8	D-11
12	12.45		4	5	5	10	D-12
13	13.45		6	10	16	26	D-13
14	14.45		9	18	22	40	D-14
15	15.45		12	24	26	50	D-15
16	16.45		14	26	24	50	D-16
17	17.45		13	27	23	50	D-17
18	18.45		18	30	20	50	D-18

LEGEND FOR BOREHOLE AND GRAIN SIZE DISTRIBUTION (BASED ON 'ASTM CLASSIFICATION D-2487')

PLASTIC CLAY | SILT | PEAT/HIGHLY ORGANIC SOIL | UNDISTURBED SAMPLE

MICACEOUS FINE SAND/SILT | SAND | SHALE | DISTURBED SAMPLE

N- BLOWS DELIVERED PER FOOT BY A 140 LB HAMMER FALLING 30 INCHES

MAX^m PENETRATION= 50 BLOWS. AFTER 50 BLOWS PENETRATION DEPTH WERE MEASURED